



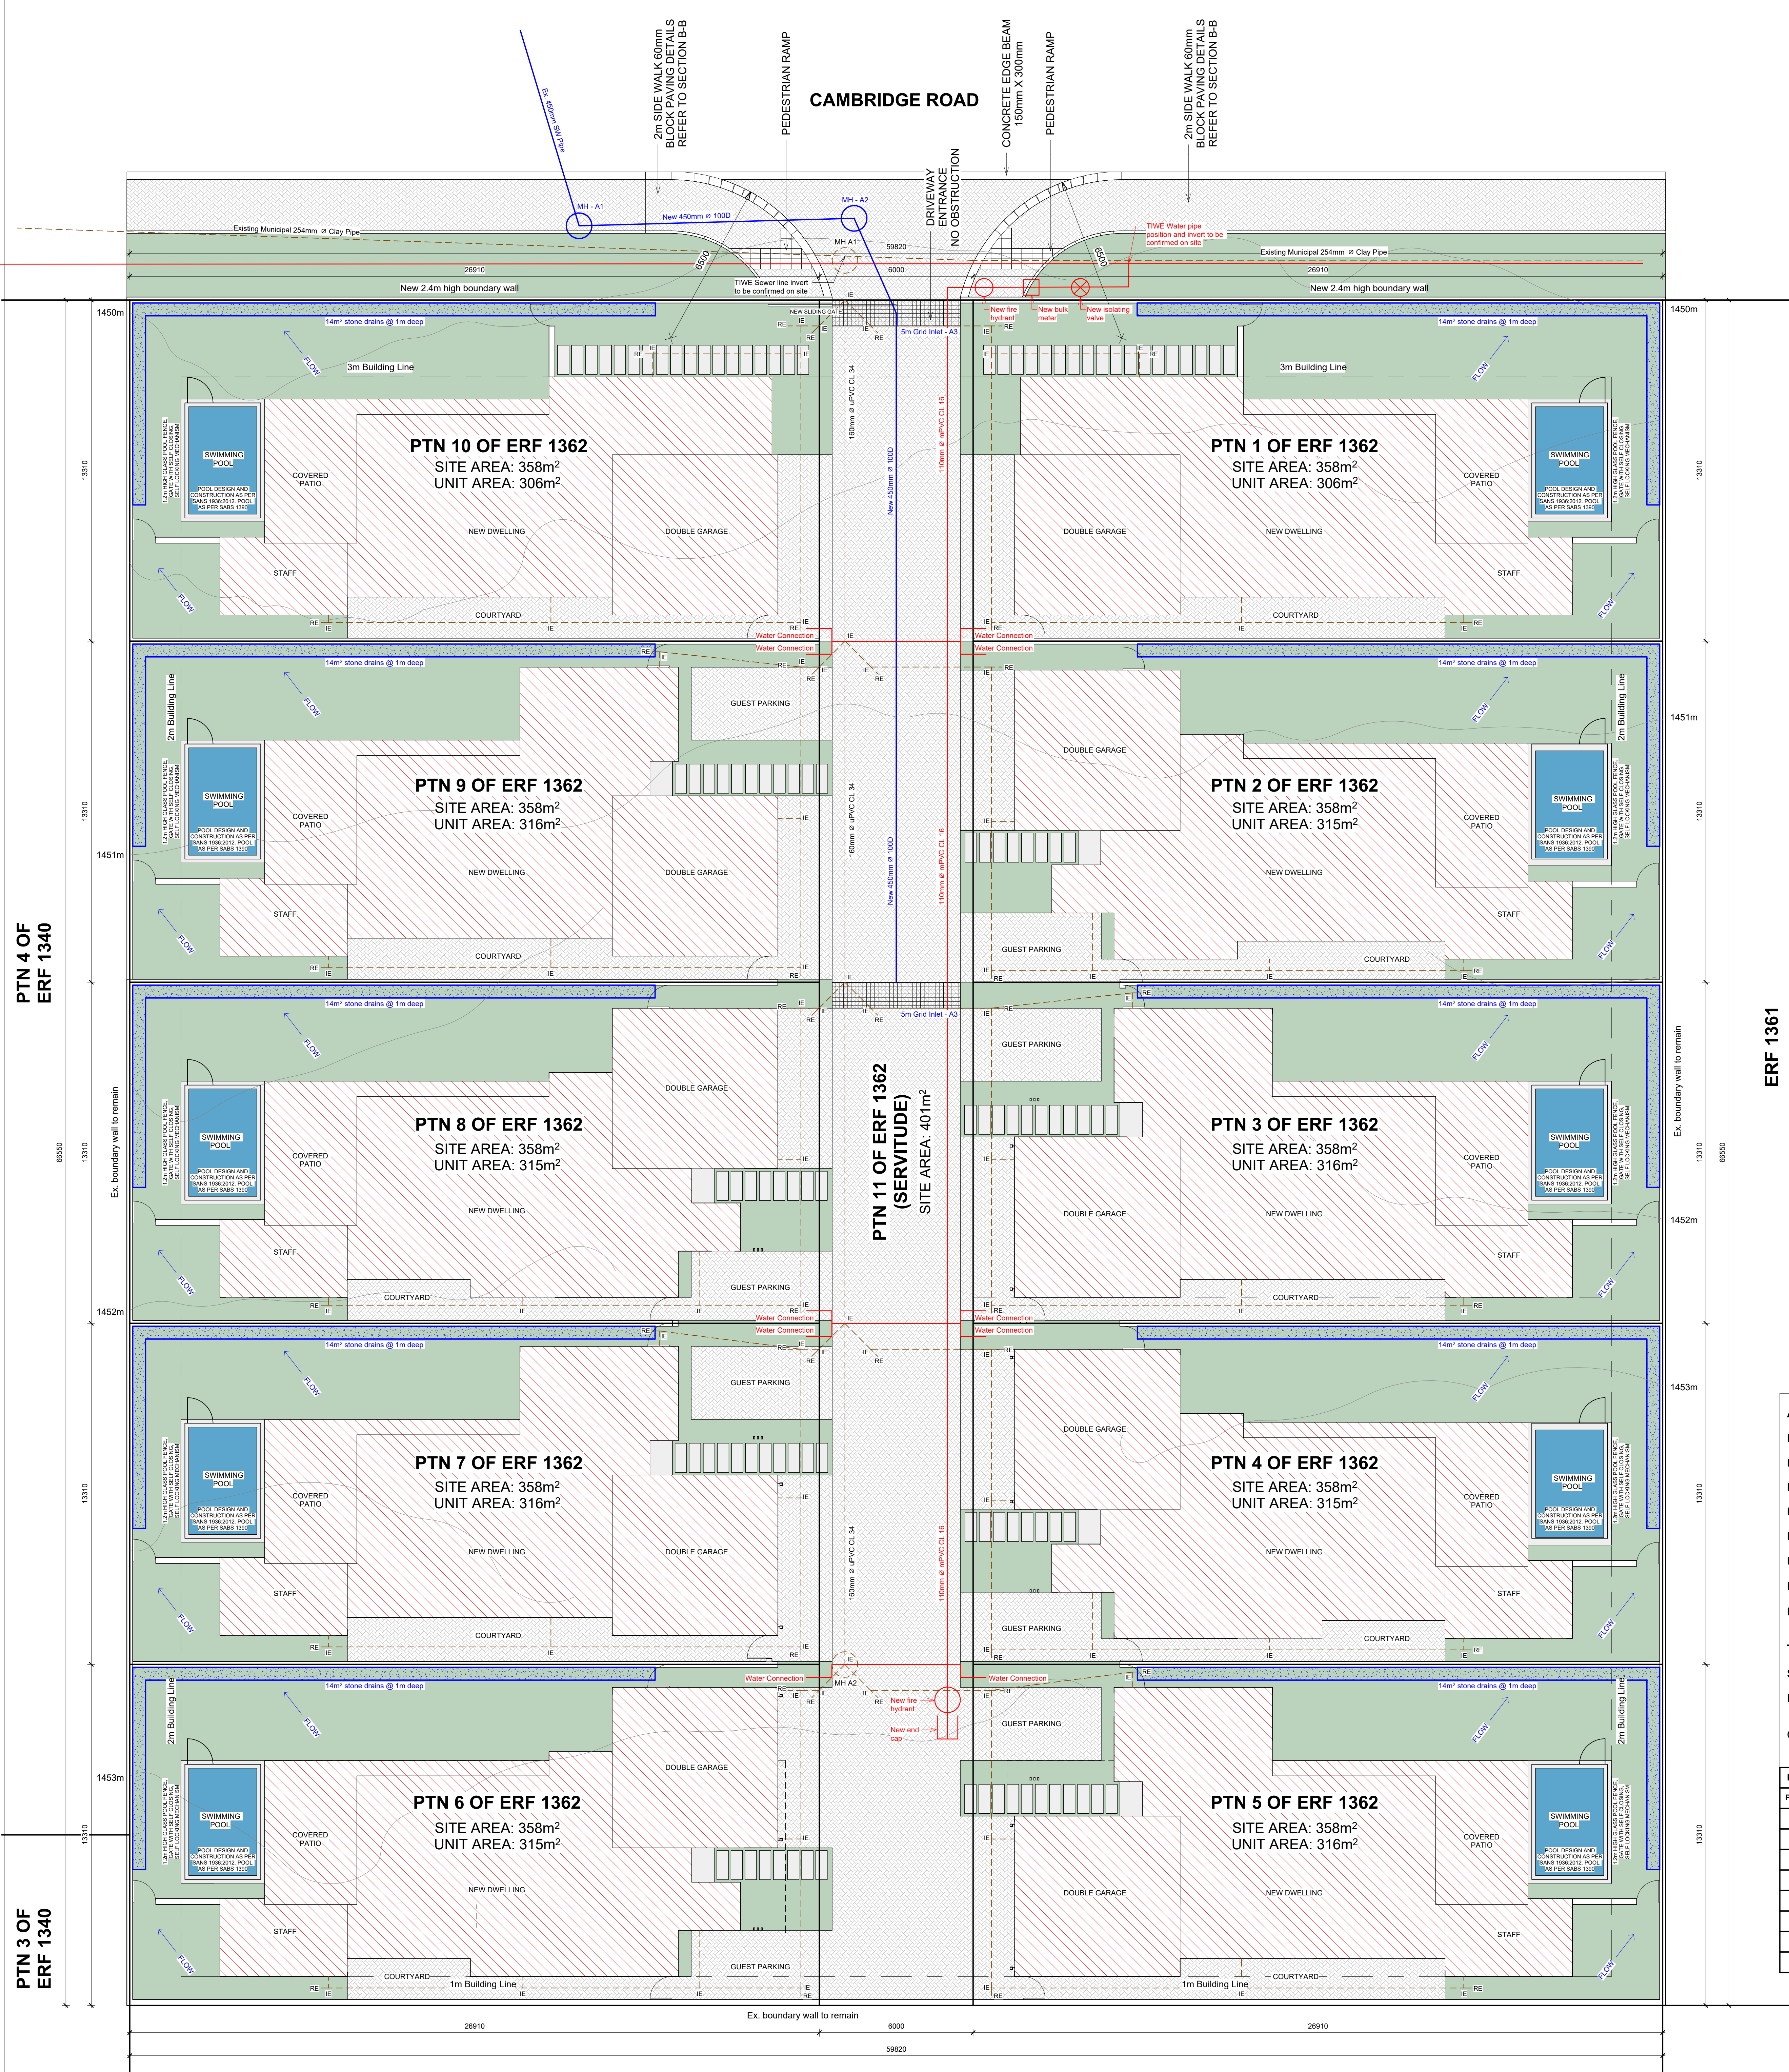


ERF 1361

ERF 1342

AREA SCHEDULE		
PTN 1:	337m²	
PTN 2:	337m²	
PTN 3:	337m²	
PTN 4:	419m²	
PTN 5:	419m²	
PTN 6:	301m²	
PTN 7:	301m²	
PTN 8:	301m²	
TOTAL AREA:		3136m²
SITE AREA:		4662m²
FAR		$\frac{3136}{4662} = 0.67$
COVERAGE		$\frac{1836}{4662} \times 100 = 39.38\%$
DEVELOPMENT CONTROL MEASURES		
PERMISSIBLE	CONTROL	ACTUAL
A	HEIGHT ZONE	A
3 STOREY	HEIGHT OF BUILDINGS	2 STOREY
70%	COVERAGE	39.38%
1:2	FLOOR AREA RATIO	0.67
	FLOOR AREA	3136
20ha	DENSITY (DWELLING UNITS PER HECTARE)	10ha
10	NO OF DWELLING UNITS ON THE ERF	10
3m- STREET 2m- SIDES	BUILDING LINES	3m- STREET 2m- SIDES

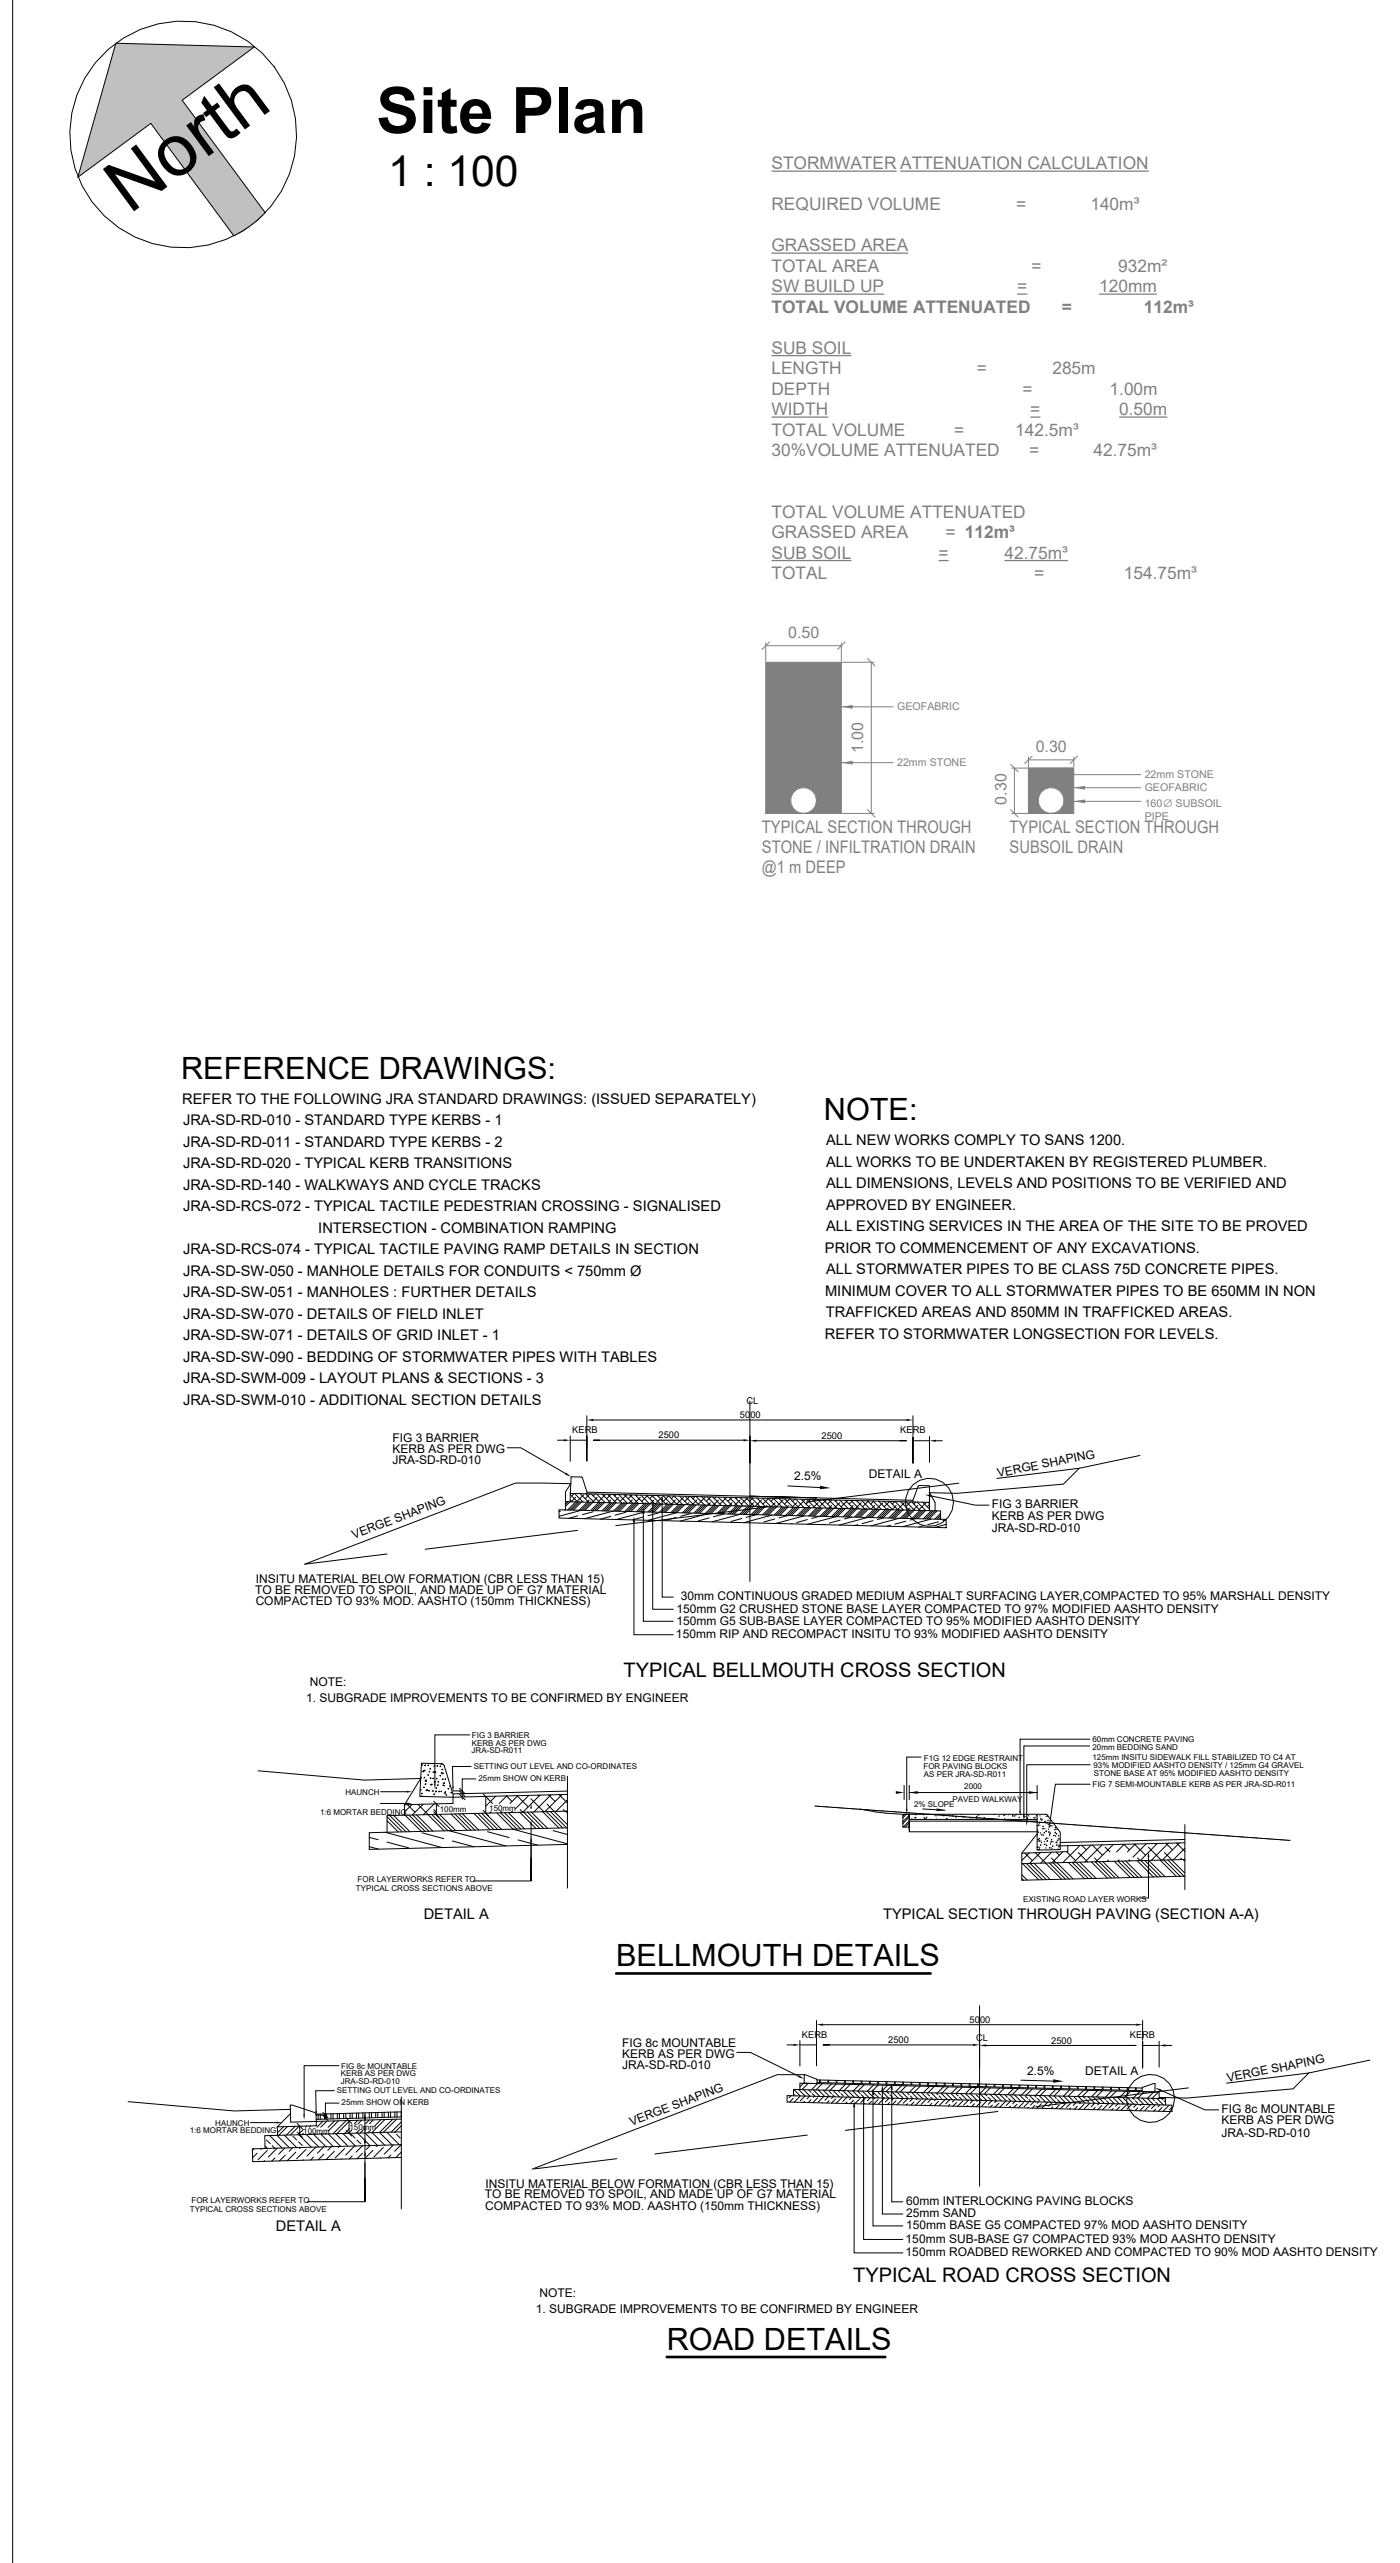

- 1) GENERAL NOTES**
- 1.2. THE NEW CUSTOMER MANAGER AT THE JOHANNESBURG WATER (PTY) LTD REGIONAL OFFICE MUST BE NOTIFIED BEFORE ANY CONSTRUCTION WORKS RELATED TO THE INSTALLATION OF WATER OR SEWER MAY BE COMMENCE.
- 1.3. ALL CONSTRUCTION WORK SHALL COMPLY WITH THE RELEVANT SABS 1200 SPECIFICATION AND JOHANNESBURG WATER (PTY) LTD SPECIFIC REQUIREMENTS.
- 1.4. ALL MATERIALS USED IN INSTALLING WATER AND SEWER MAINS SHALL COMPLY WITH THE RELEVANT SABS SPECIFICATION AND WITH THE MINIMUM REQUIREMENTS OF JOHANNESBURG WATER (PTY) LTD.
- 1.5. THE POSITION AND DEPTH OF ALL EXISTING SERVICES ON THE SITE AND OFF THE SITE WHERE AFFECTED BY THE WORKS SHALL BE CONFIRMED PRIOR TO ANY CONSTRUCTION WORK ON THE INSTALLATION OF WATER OF SEWER MAINS BEING COMMENCED.
- 1.6. ONLY JOHANNESBURG WATER (PTY) LTD STAFF SHALL CARRY OUT TIE-IN CONNECTIONS TO EXISTING WATER AND SEWER MAINHOLES AND MAINS. NOTE THAT A MINIMUM OF 2 WEEKS NOTICE SHALL BE GIVEN TO JOHANNESBURG WATER (PTY) LTD STAFF TO ATTEND SITE INSPECTIONS, MEETING AND ANY OTHER NECESSARY ON SITE LIAISON.
- 1. SPECIFIC WATER REQUIREMENTS**
- 1.2. PROTECTION OF FITTINGS AND MAINS;
- 1.2.1. STEEL MAINS: COPON LINED AND SUITABLY WRAPPED PER SPECIFICATION.
- 1.2.2. STEEL FITTINGS: COPON COATED INTERNALLY AND SUITABLY WRAPPED PER SPECIFICATION.
- 1.2.3. GALVANISED FITTINGS: SUITABLY WRAPPED PER SPECIFICATION.
- 1.3. ALL VALVE AND BELOW GROUND HYDRANT CHAMBERS TO BE WATERTIGHT.
- 1.4. POSITION OF ACROSS THE ROAD ERF CONNECTIONS TO BE MARKED BY A W CUT INTO THE KERBSTONE.
- 1.5. THE CONTRACTOR SHALL NOT OPERATE ANY WATER VALVE OR OTHER FITTINGS WITHOUT THE PERMISSION OF JOHANNESBURG WATER (PTY) LTD.
- 1.6. COVER TO WATER MAINS;
- THE DEPTHS LISTED ARE DEPTHS TO FINAL GROUND LEVEL **INCLUSIVE OF ANY LANDSCAPING** UNDERTAKEN ON THE SITE.
- | | Minimum (mm) | Maximum (mm) |
|-----------------|--------------|--------------|
| Gravel Road | 1000 | 1500 |
| All other areas | 800 | 1500 |
- 1.7. ALL WATER MAINS ARE TO BE INSTALLED AT 2 METERS FROM ERF BOUNDARIES UNLESS OTHERWISE SHOWN ON THE DRAWING.
- 1.8. ANY ANCHOR BLOCKS CONSTRUCTED ARE TO PROPERLY SHUTTERED AND CAST AGAINST UNDISTURBED GROUND. ANY OVER EXCAVATION IS TO BE FILLED WITH MASS CONCRETE.
- SPECIFIC SEWER REQUIREMENTS**
2. ALL MATERIALS SHALL COMPLY WITH THE RELEVANT SABS SPECIFICATION AND WITH THE REQUIREMENTS OF JOHANNESBURG WATER (PTY) LTD.
3. SEWERS LAID AT GRADIENTS STEEPER THAN 1:12 SHALL BE ANCHORED AT THE JOINTS WITH PROPERLY DESIGNED ANCHOR BLOCKS. CONCRETE OF STRENGTH 15MPa (1:3:6) SHALL BE USED FOR ANCHOR BLOCKS. NO TREES OR SHRUBS SHALL BE PLANTED WITHIN 2 METERS OF ANY SEWER MAIN.
4. SEWER MANHOLES ARE TO BE SPACED A MAXIMUM DISTANCE OF 80 METERS.

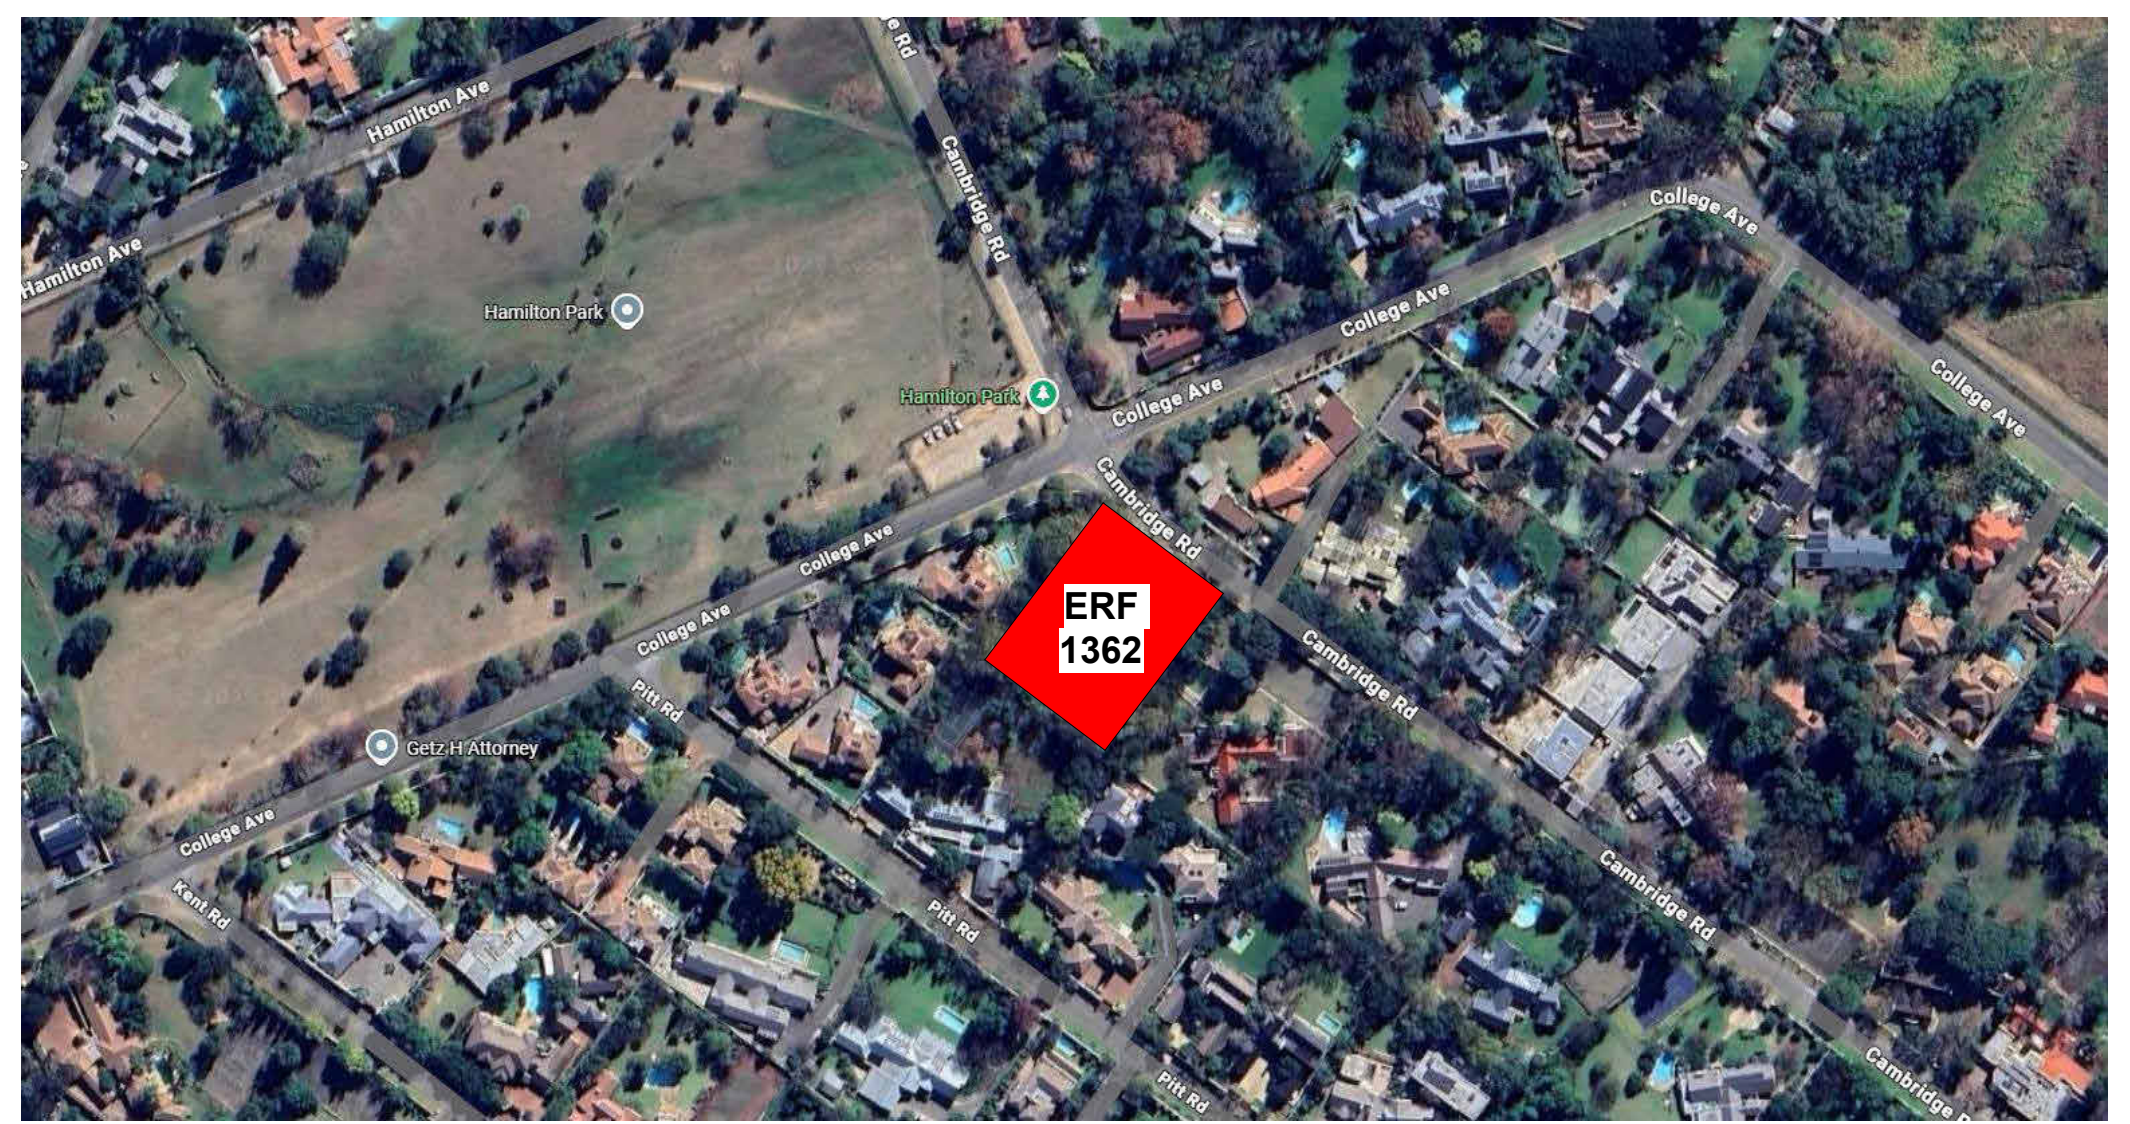

Locality Plan

I hereby approve this drawing (i) for the design contained herein and (ii) for submission to the local authority for approval

ENGINEER'S SIGNATURE: _____ DATE: _____

ARCHITECT'S SIGNATURE: _____ DATE: _____

I hereby approve this drawing (i) for the design contained herein and (ii) for submission to the local authority for approval

OWNER'S SIGNATURE: _____ DATE: _____

COPYRIGHT Chris Sparks Architecture

This drawing and the copyright therein belong to Chris Sparks and the drawing may not be reproduced in any form without the written permission of Chris Sparks.

CHRIS SPARKS Architects

TEL: +27 83 788 6312
Email: chris@chris-sparks.co.za
2026/02/09

11 Forbes Street, Johannesburg

Client: GAVIN & JENNIFER JUNE JULYAN

Project: NEW RESIDENTIAL DEVELOPMENT ON ERF 1362, BRYANSTON

Drawing Description: SDP - SITE PLAN

Scale: B1 DATE: 2026/02/09 DRAWN BY: CS, LF PROJ REV: 1: 100

DRAWING NUMBER: 01